

锦屏磷矿工厂更新设计


设计说明

本次设计选址在江苏省连云港市锦屏镇锦屏磷矿，是历经近20年的项目，锦屏磷矿开采了近100年，后由于资源枯竭停止开采，锦屏磷矿也随之废弃至今。该磷矿曾经代表着连云港市的工业辉煌，承载着人们的回忆，所以锦屏磷矿的改造非常必要。

在此之前对场地进行了考察，并植入了“城市双修”的理念。在锦屏磷矿改造整个规划方面，公园设置了一条主要景观轴线和特色火车轨道及健康步道，形成一轴两环的布局；以工厂遗址为中心，结合周边绿地设置教育科普区、生态体验探险区、有纪念意义的休闲区、休闲区、瞭望台共五个功能区；园区中道路系统分为三级。公园的景观设计强调表达场地的生态性、工业文化特征，设有教育科普区景观节点、生态体验探险区景观节点、有纪念意义的休闲区景观节点3个主要节点，并对5个景观节点予以详细说明。在专项设计方面，考虑到公园的竖向分析、植物种植设计与景观小品以及导视系统的设置。

周边景观

区位分析

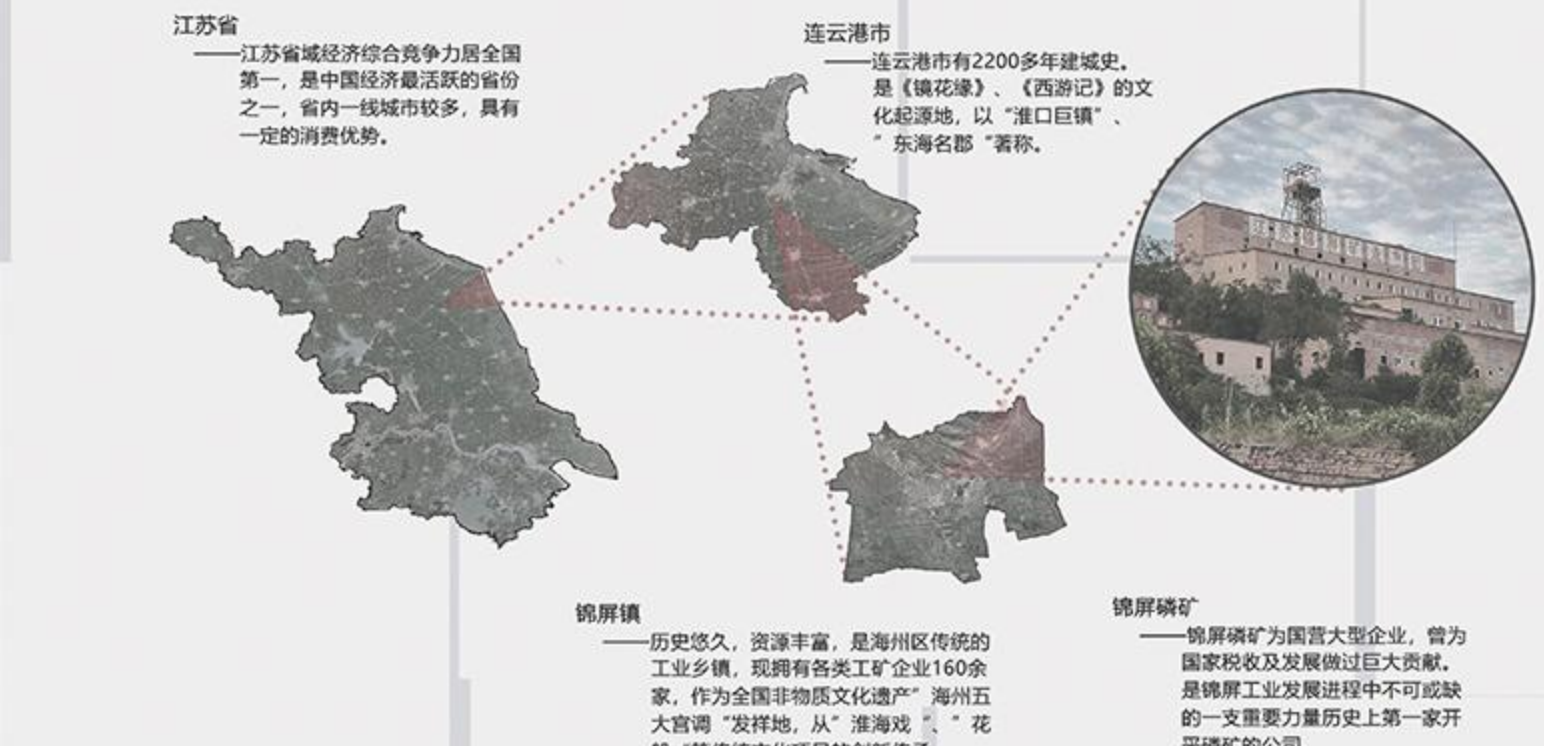

场地现状




景观植被遭到破坏，岩石裸露，杂草丛生

历史遗迹遗留




场地遗留建筑部分遭到人为破坏


景观规划结构

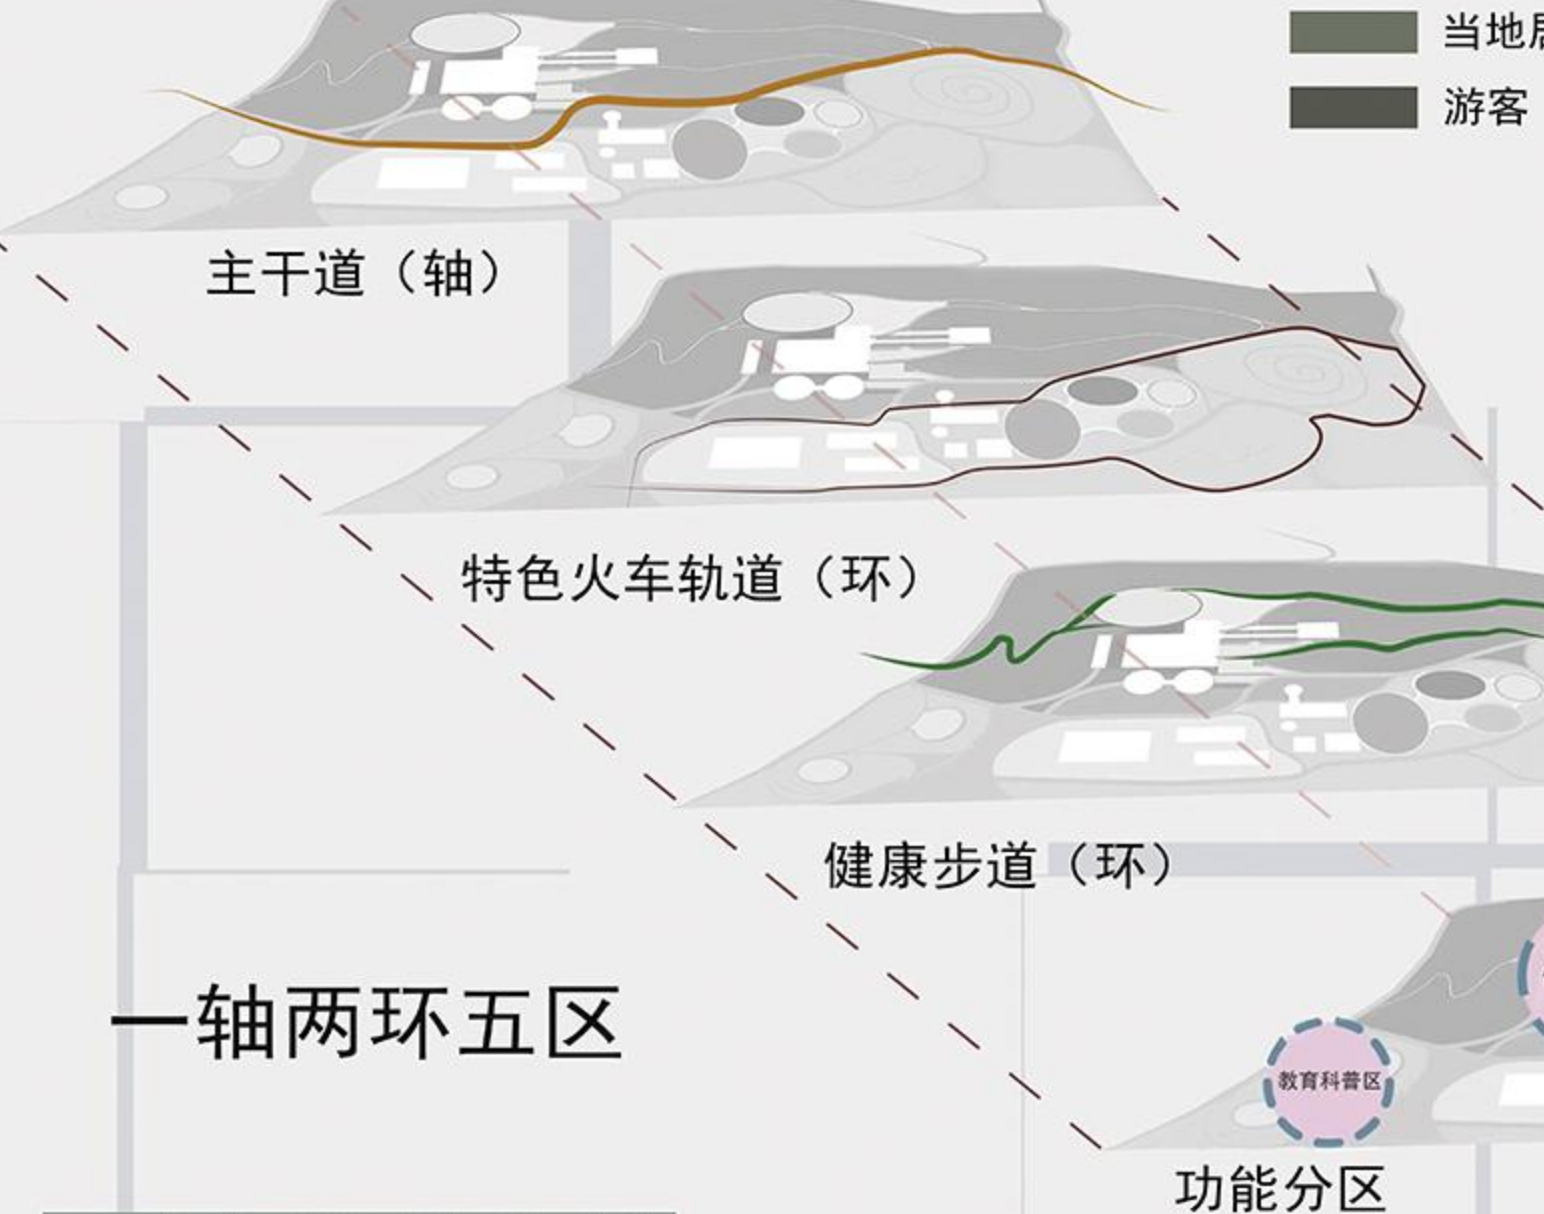


交通流线分析

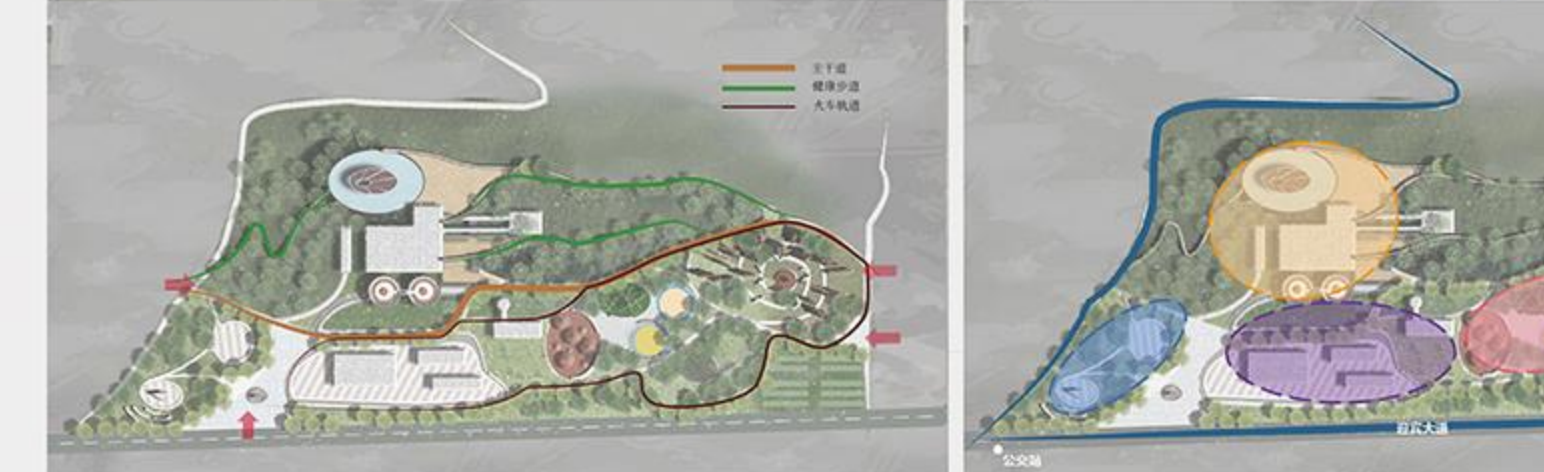


剖面图

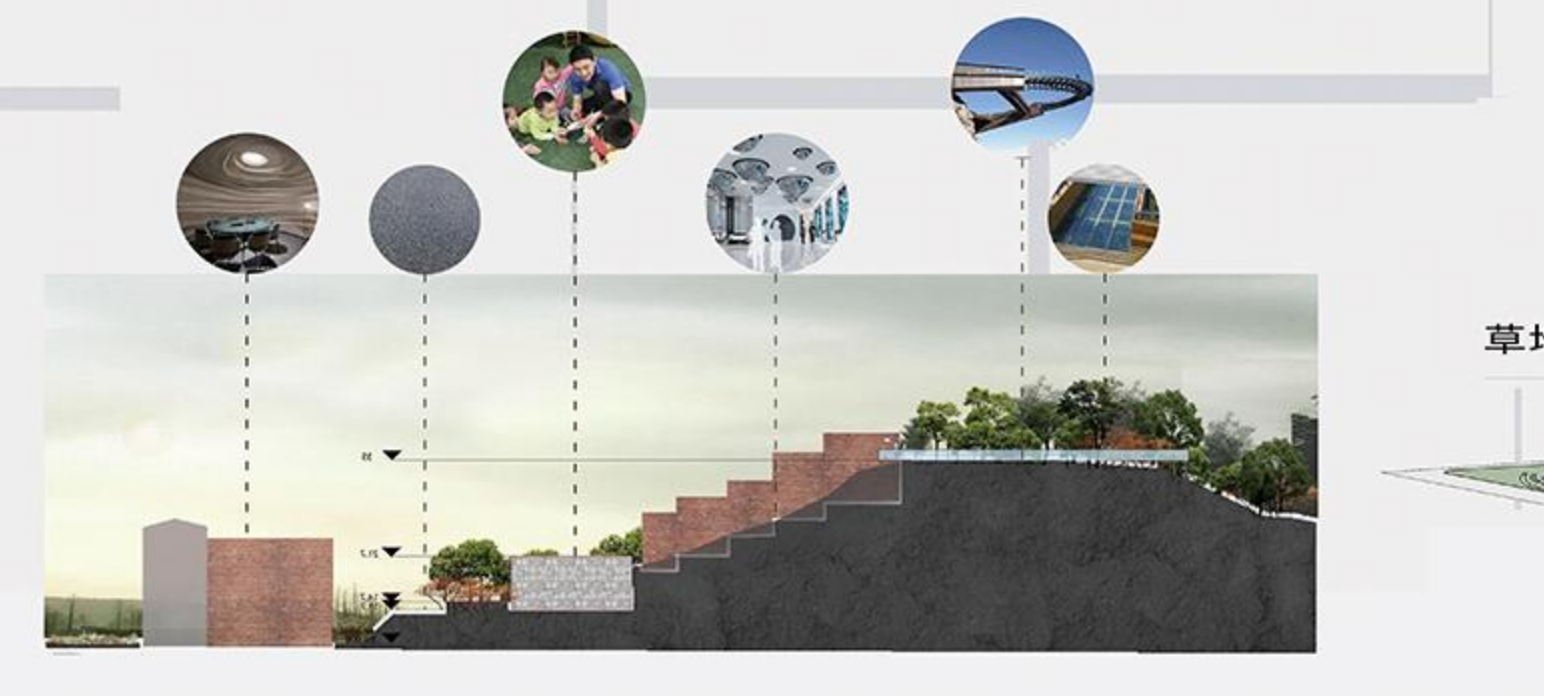


功能需求分析

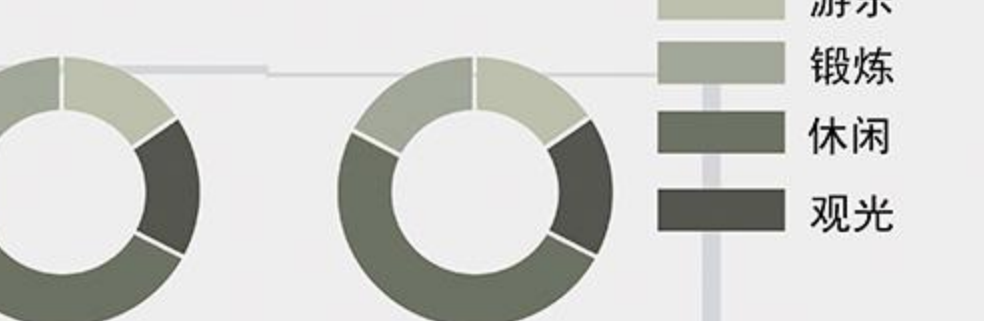


景观节点视线

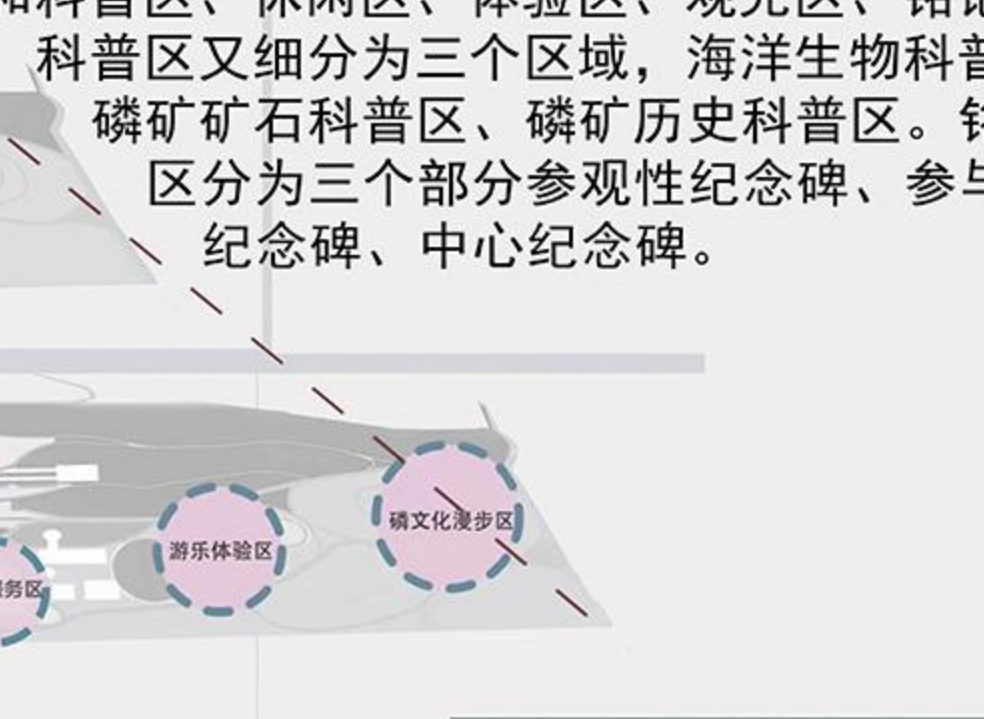

场地结构分析

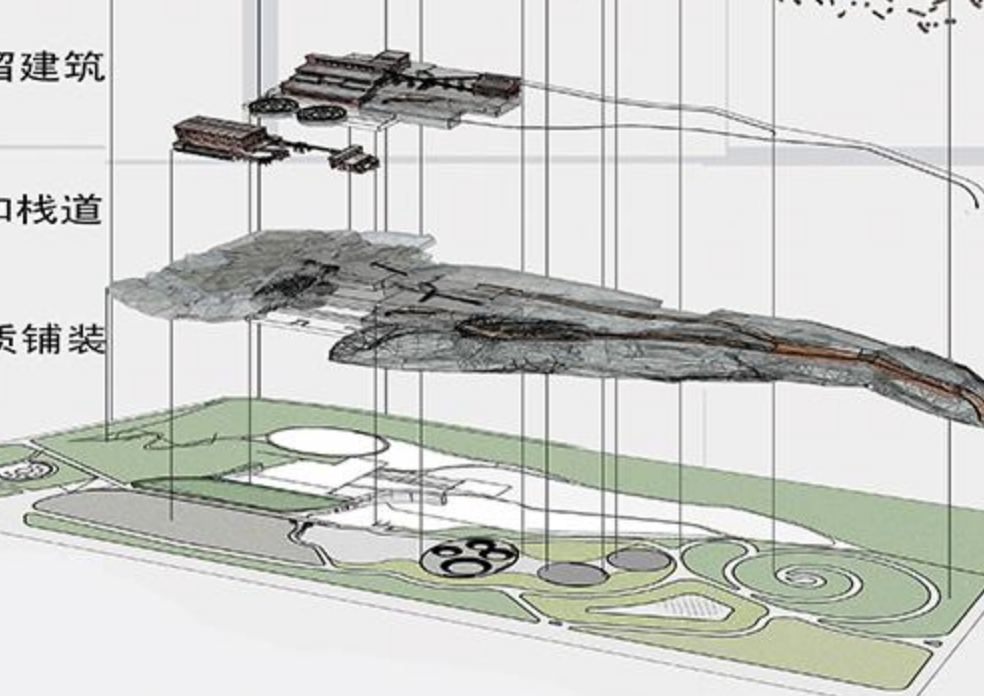

景观小品设计

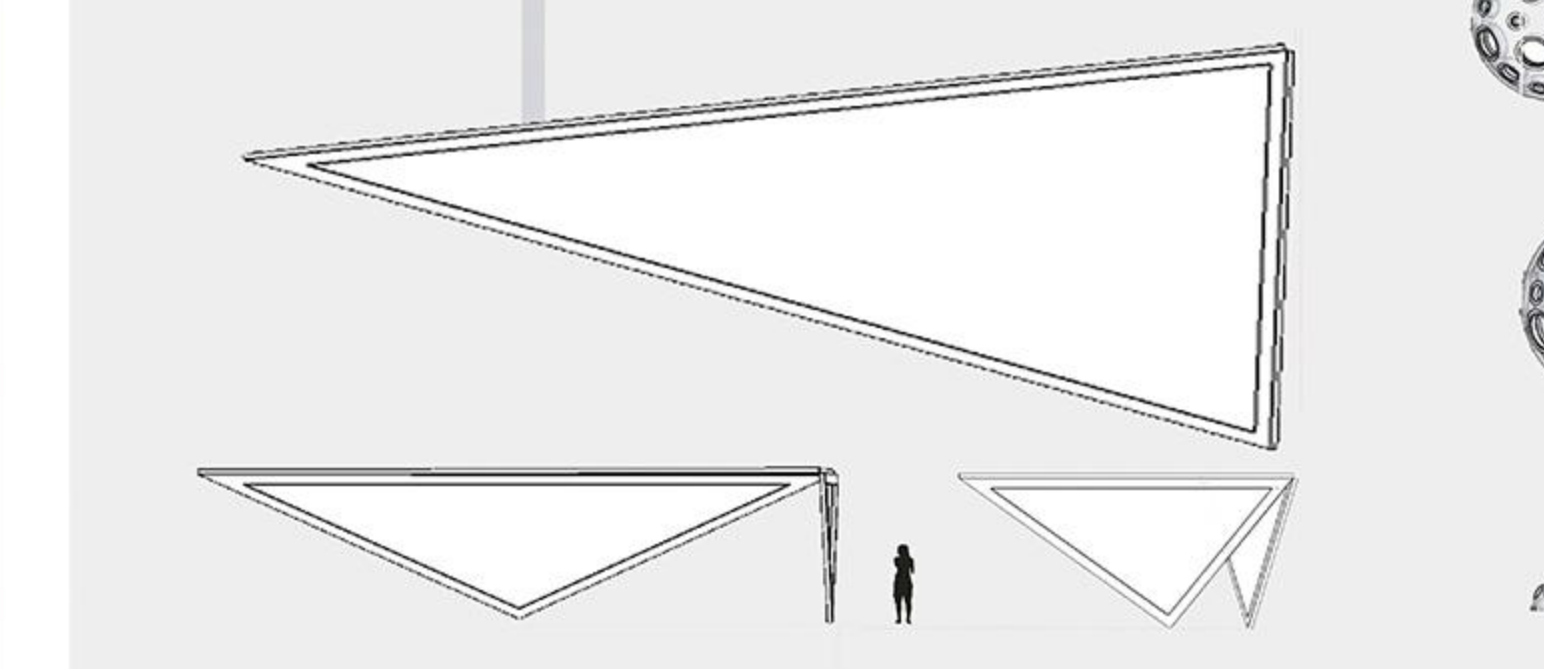

植物配置分析




导视设计及效果图



彩平图



设计构思

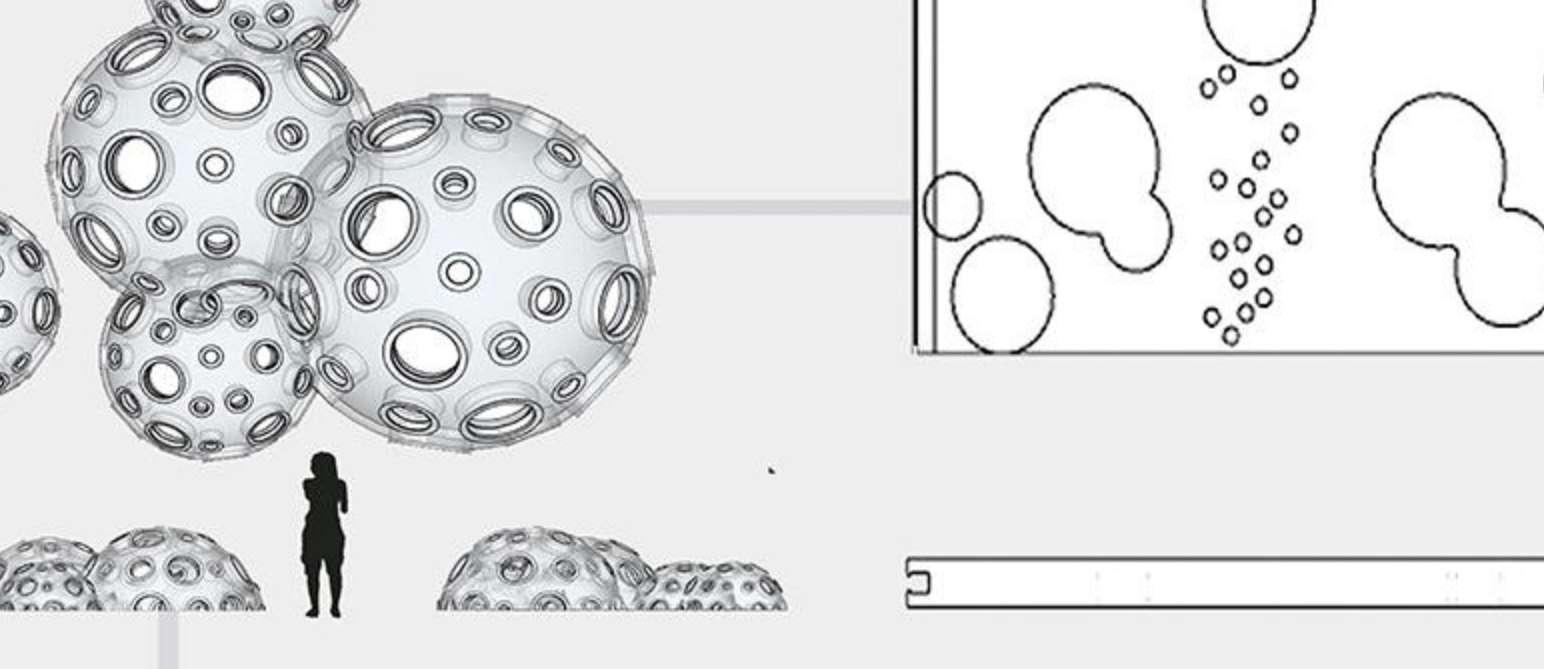


剖面图



效果图



物理空间更新设计

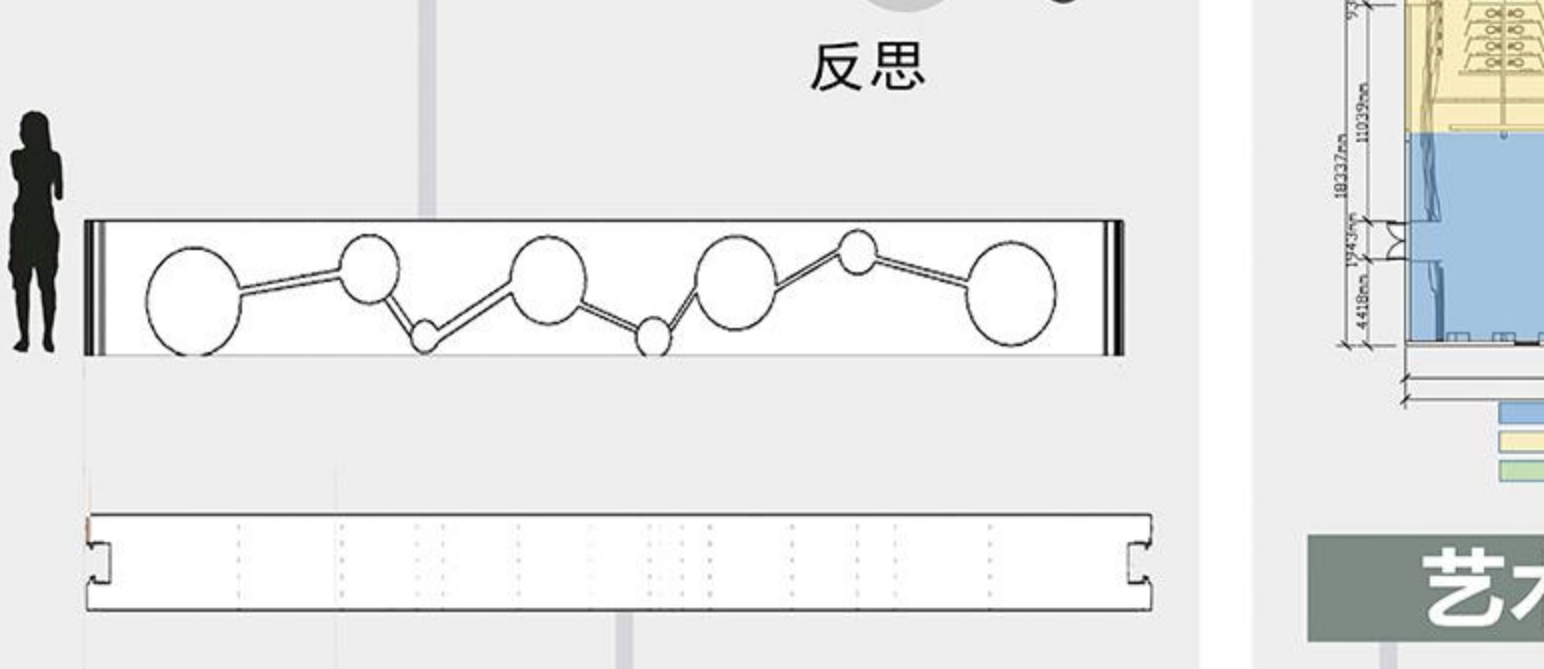

平面图



艺术装置设计



效果图

